


4

3



2

1


Bottom view of Base Section

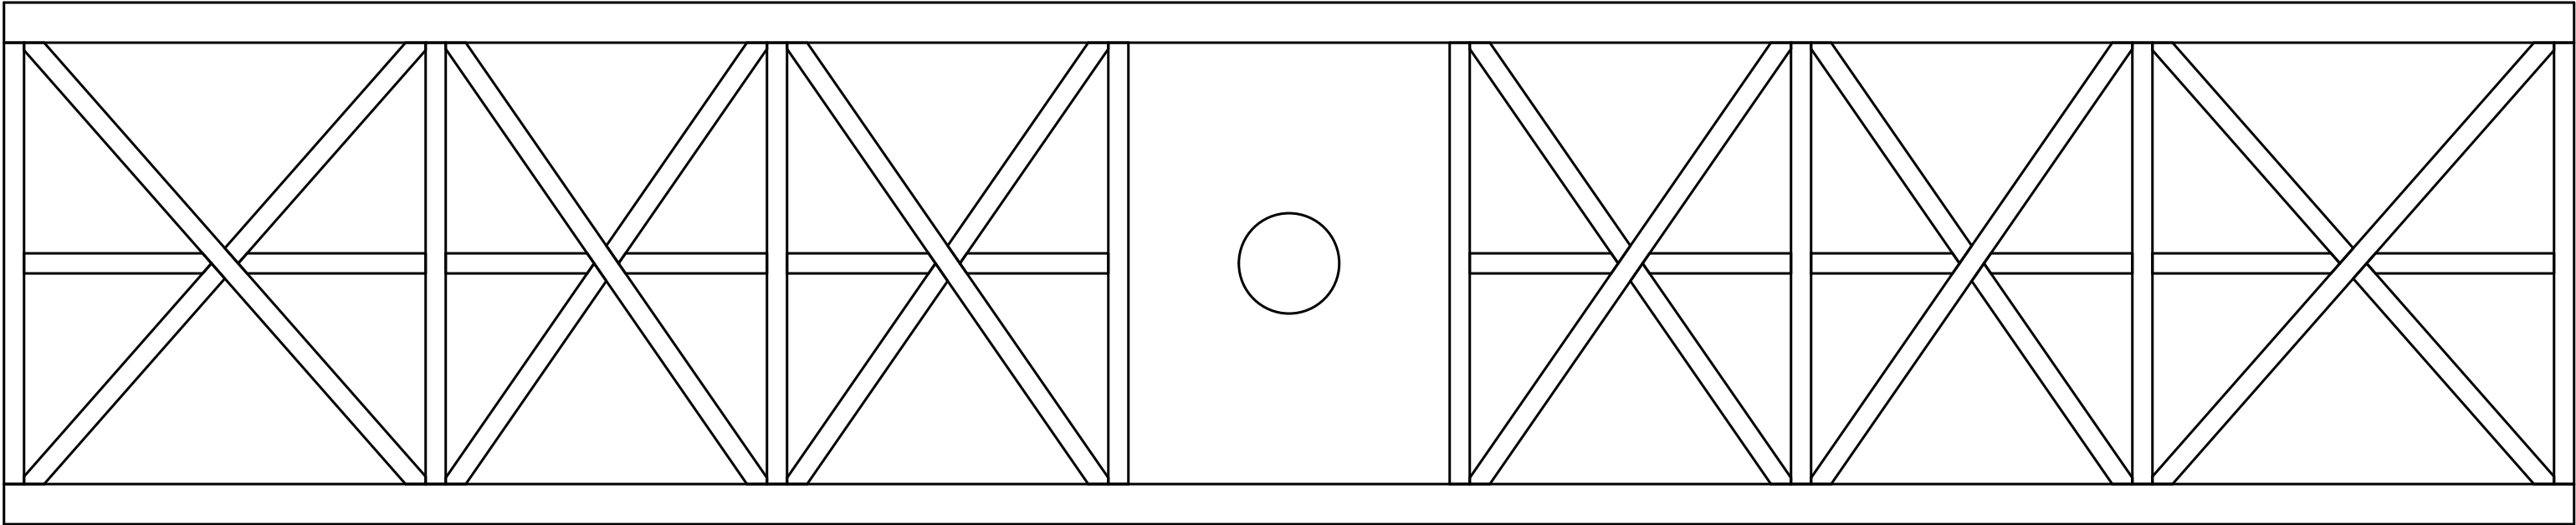

Top View of Top Section

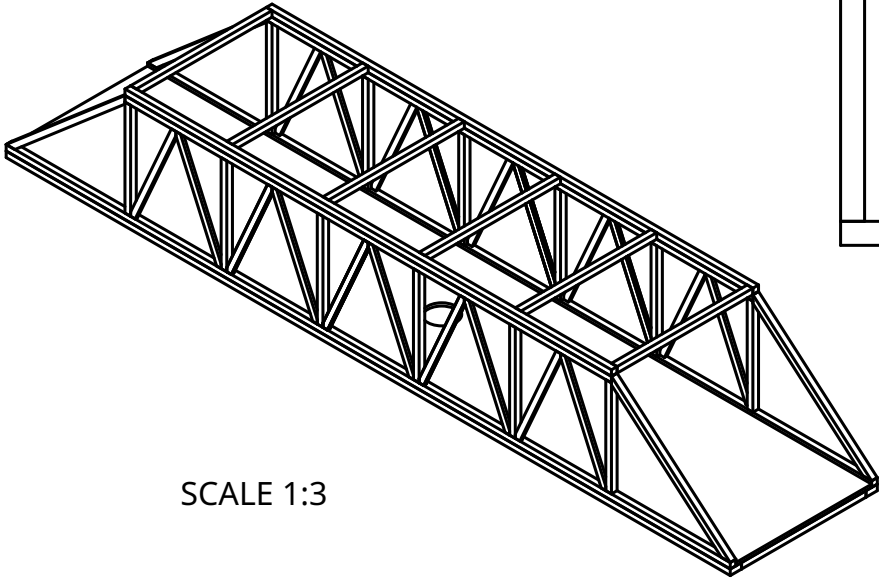 

SCALE 1:3

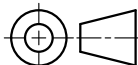UNLESS OTHERWISE SPECIFIED, DIMENSIONS ARE IN INCHES .XX = ±.0- .XXX = ±.00- .XXXX = ±.000- SURFACE FINISH 	NAME		DATE	TITLE Team 401A Model Road Bridge Engineering Design					
	DRAWN		MANASVINI KALA					10/31/2020	
	CHECKED								
	APPROVED								
DO NOT SCALE DRAWING					SIZE B				
BREAK ALL SHARP EDGES AND REMOVE BURRS									
THIRD ANGLE PROJECTION									
	MATERIAL		FINISH		DWG NO.		REV. C		
	Balsa		Natural		Blueprint 2				
					SCALE	1:1	WEIGHT	SHEET	1 of 1

4

3

2

1